A1

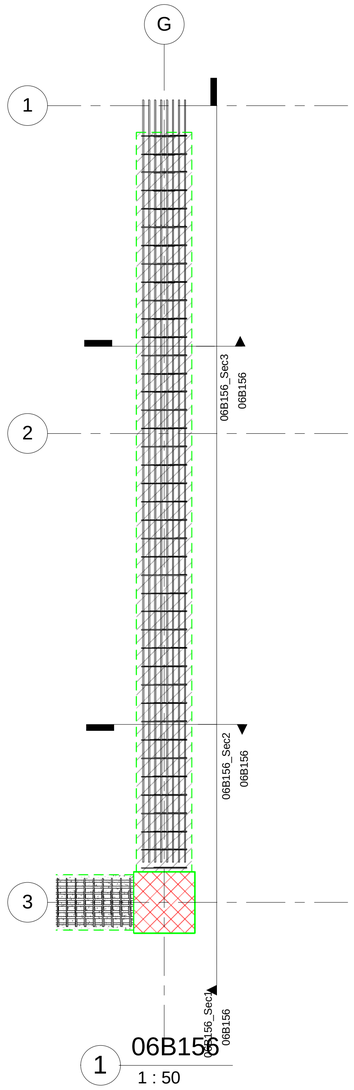

1 06B156
1 : 50

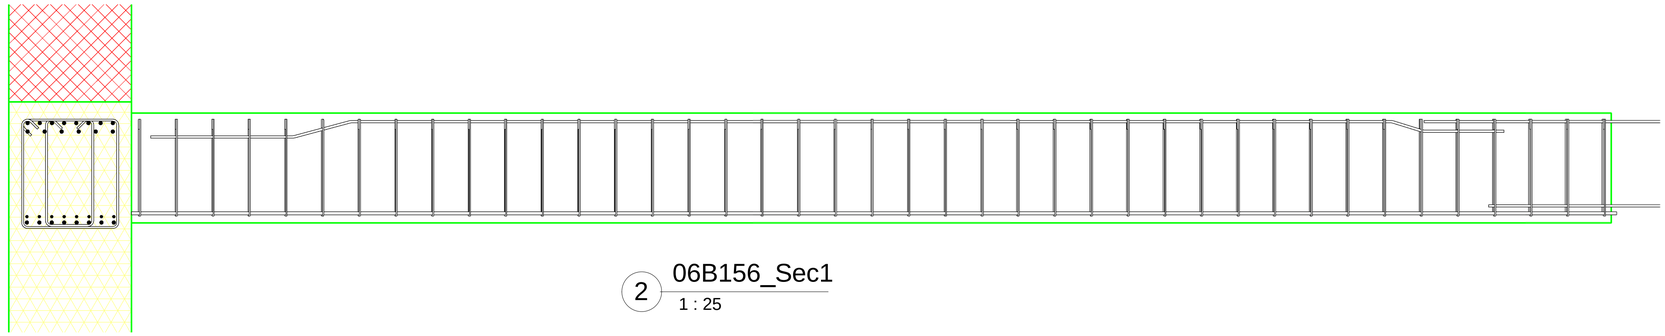

2 06B156_Sec1
1 : 25

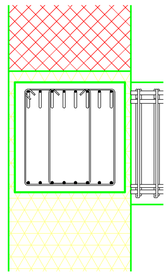

3 06B156_Sec2
1 : 25

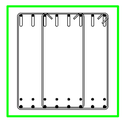

4 06B156_Sec3
1 : 25

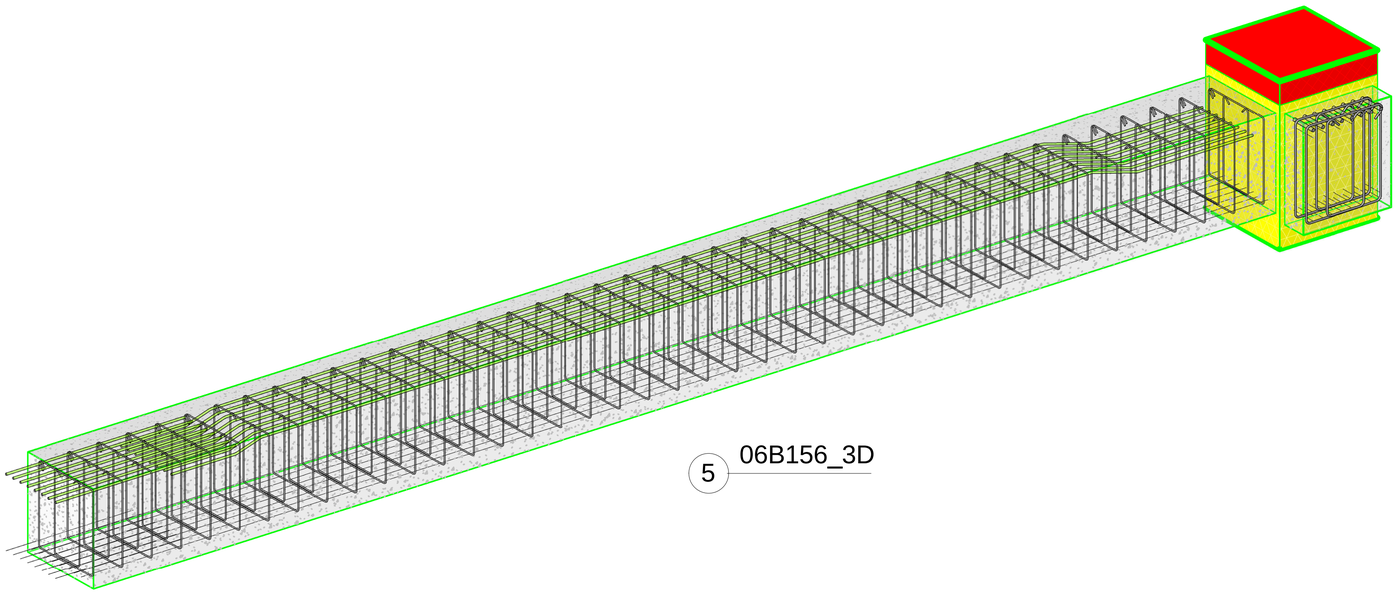

5 06B156_3D

STRUCTURAL MODELLING TEST

Main Contractor :

SHIMIZU CORPORATION
8 Kallang Ave. #05-01 Aperia Tower 1, S339509
Tel: (65) 6220 0406 Fax: (65) 6224 9890
ncc-pjt.sg@shimz.biz www.shimz-global.com

Drawing Description :

Rebar Details

FILENAME : \\192.168.1.3\3.Drawing_DB\100 Public Folder\For Rebar Interns\Rebar Reference Drawings\z Question\Answer\REBAR_TEST_Answer.rvt

SCALE :	DATE : 11/09/18	REV.
DRAWN : Author	CHECKED : Checker	

DRAWING NO. : 06B156

TEST

PRINTED ON : 9/11/2018 6:05:03 PM